AREA	SQ-M
TOTAL AREA	230

GENERAL NOTES:

1. VERIFY ACTUAL SITE CONDITION FOR THE EXACT DIMENSIONS AND INFORMATION OF ALL AREAS AND BUILT-IN FURNITURES AND LOOSE FIXTURES INDICATED IN THE DWGS.
2. CONTRACTOR TO COORDINATE ALL M&E,C&S WORKS AND HIGHLIGHT ALL DISCREPANCIES TO ID PRIOR TO CONSTRUCTION.
3. SITE MARKING OF PARTITIONS TO BE CONFIRMED BY ID CONTRACTOR PRIOR TO INSTALLATION.
4. CONTRACTOR TO CLARIFY ANY DISCREPANCIES BETWEEN CONSULTANTS DRAWINGS
5. FLOOR LEVEL & CEILING HGT WILL ADAPT TO SITE CONDITION.

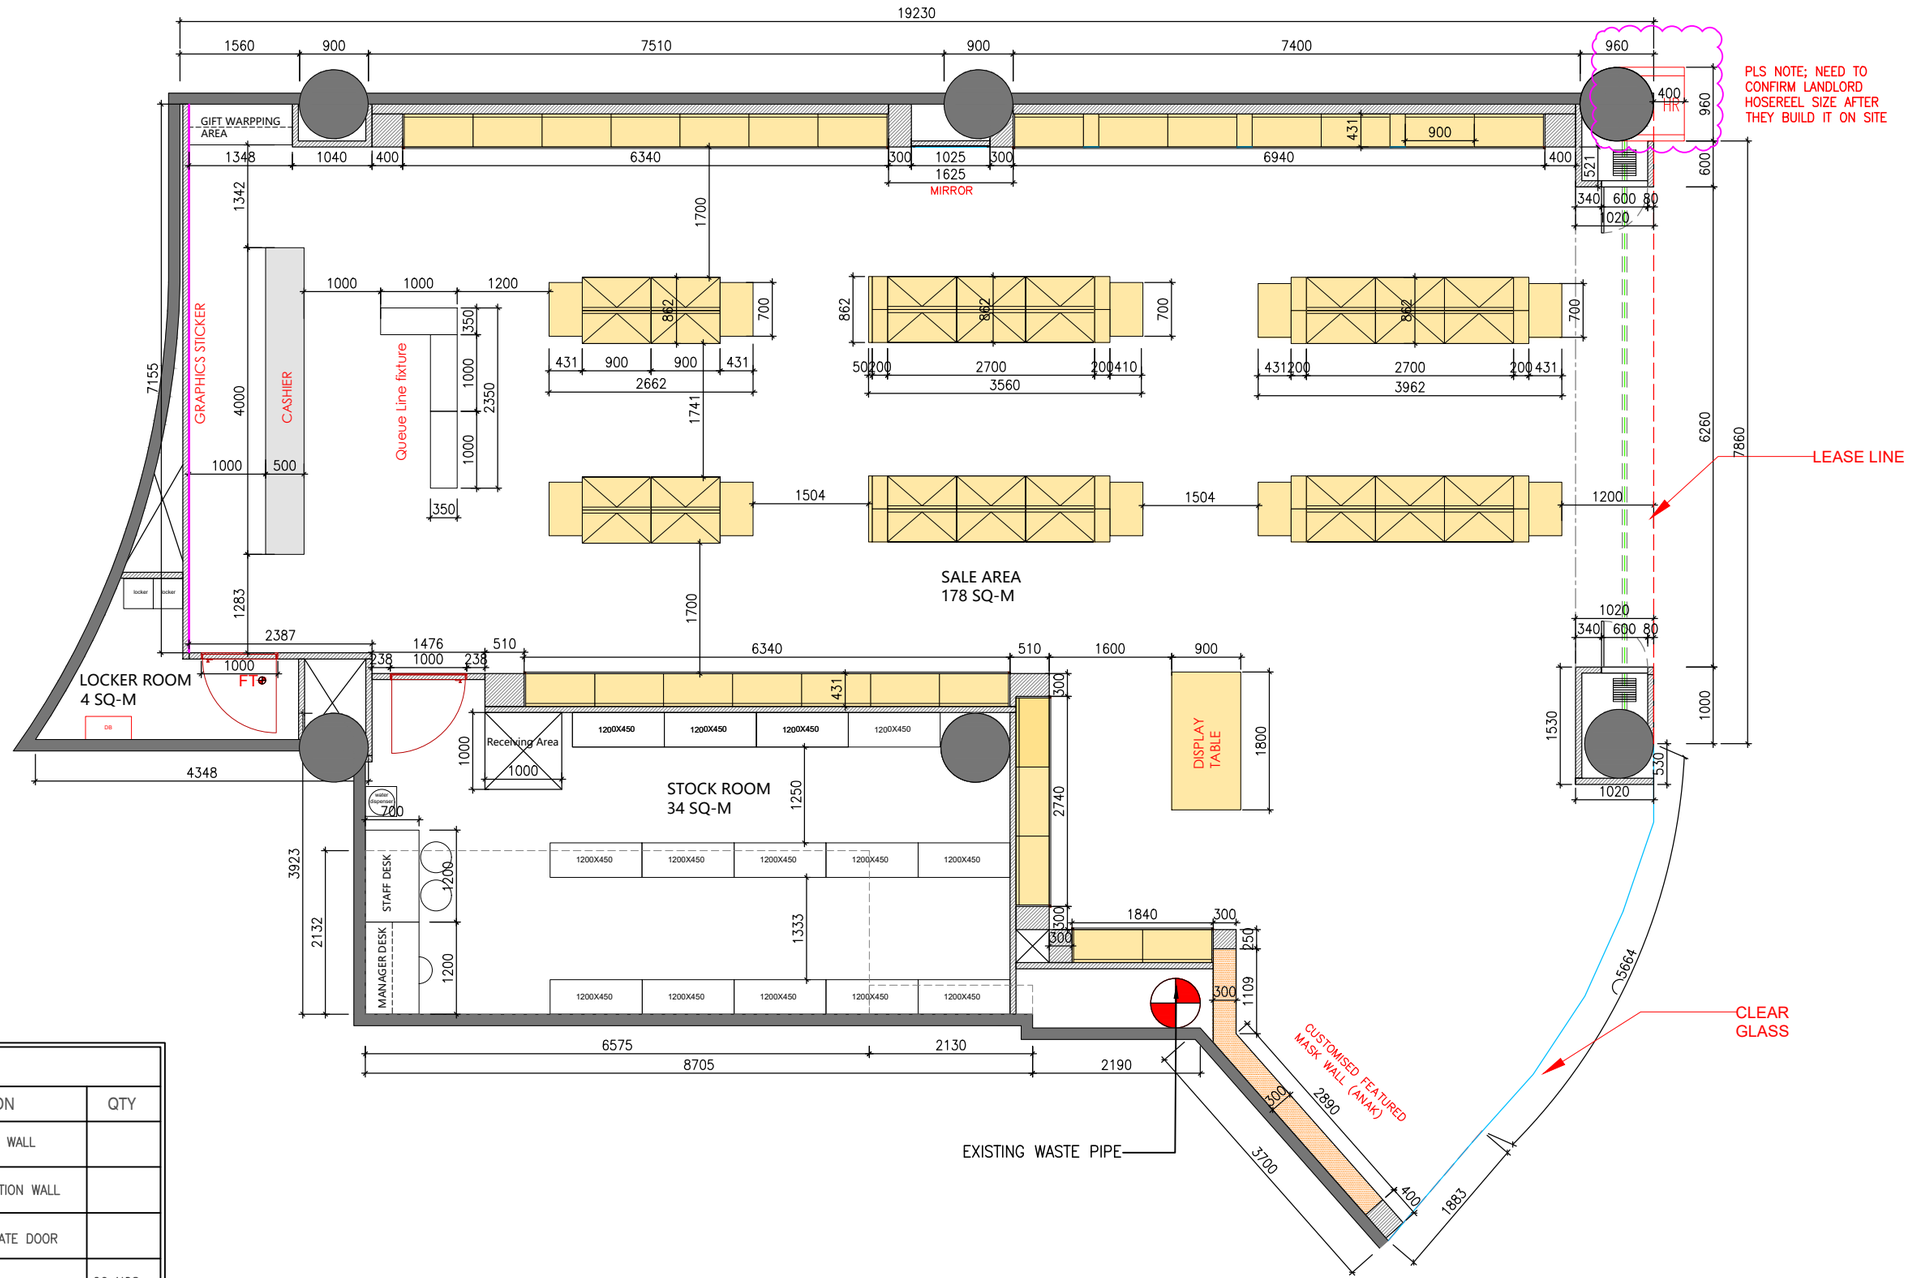

LEGEND:		
SYMBOL	DESCRIPTION	QTY
	EXISTING STRUCTURE WALL	
	NEW BUILT-IN PARTITION WALL	
	BIFOLD POLYCARBONATE DOOR	
	WALLBAY (W900XD431)	26 NOS
	2 BAY GONDOLA+ENDCAP (W2662XD862)	2 NOS
	3 BAY GONDOLA+ENDCAP+HYGIENE (W3962XD862)	4 NOS

STOCK ROOM	
RACKING	QTY
1200x450	14 NOS

01 FURNITURE PLAN

SCALE 1 : 80

Rev	Date	Description

Client:

Project :

FRAN @ BUGIS+

(#01-04)

Project Management:

Studio J Solutions Pte. Ltd

email : enquiries@studioj.sg
web : www.studioj.sg
Add : 7 Mandai Link
#03-20 Mandai Connection
Singapore 728653

Design Consultant:

Main Contractor:

Studio J Solutions Pte. Ltd

email : enquiries@studioj.sg
web : www.studioj.sg
Add : 7 Mandai Link
#03-20 Mandai Connection
Singapore 728653

Mechnical & Electrical Consultant:

Structural Engineer:

General Notes:

COPYRIGHT OF ALL DESIGNS AND DATA SHOWN IN THIS DRAWING IS RETAINED BY STUDIO J SOLUTION PTE.LTD. WRITTEN PERMISSION IS REQUIRED FOR ANY USE AND/OR REPRODUCTION. ALL PRINTS, SPECIFICATIONS AND COPYRIGHTS ARE THE PROPERTY OF STUDIO J SOLUTION PTE.LTD AND SHALL BE RETURNED ON COMPLETION OF WORKS. ALL MEASUREMENTS MUST BE CHECKED AT SITE BY THE CONTRACTOR AND NOTIFICATION TO BE MADE TO THE DESIGNER BEFORE COMMENCEMENT OF WORK IN THE EVENT OF ANY DISCREPANCIES ARISING FROM THE DRAWINGS. ALL DRAWINGS MUST BE READ IN CONJUNCTION WITH OTHER CONSULTANT DRAWINGS.

Drawn : WILLIAM

Checked: JF

Approved:

First submission date:

Scale : A3 AS SHOWN

Drawing Title:

LAYOUT PLAN

Drawing Number:

PL-01

Project Number:

FRAN_BUGIS+_020726